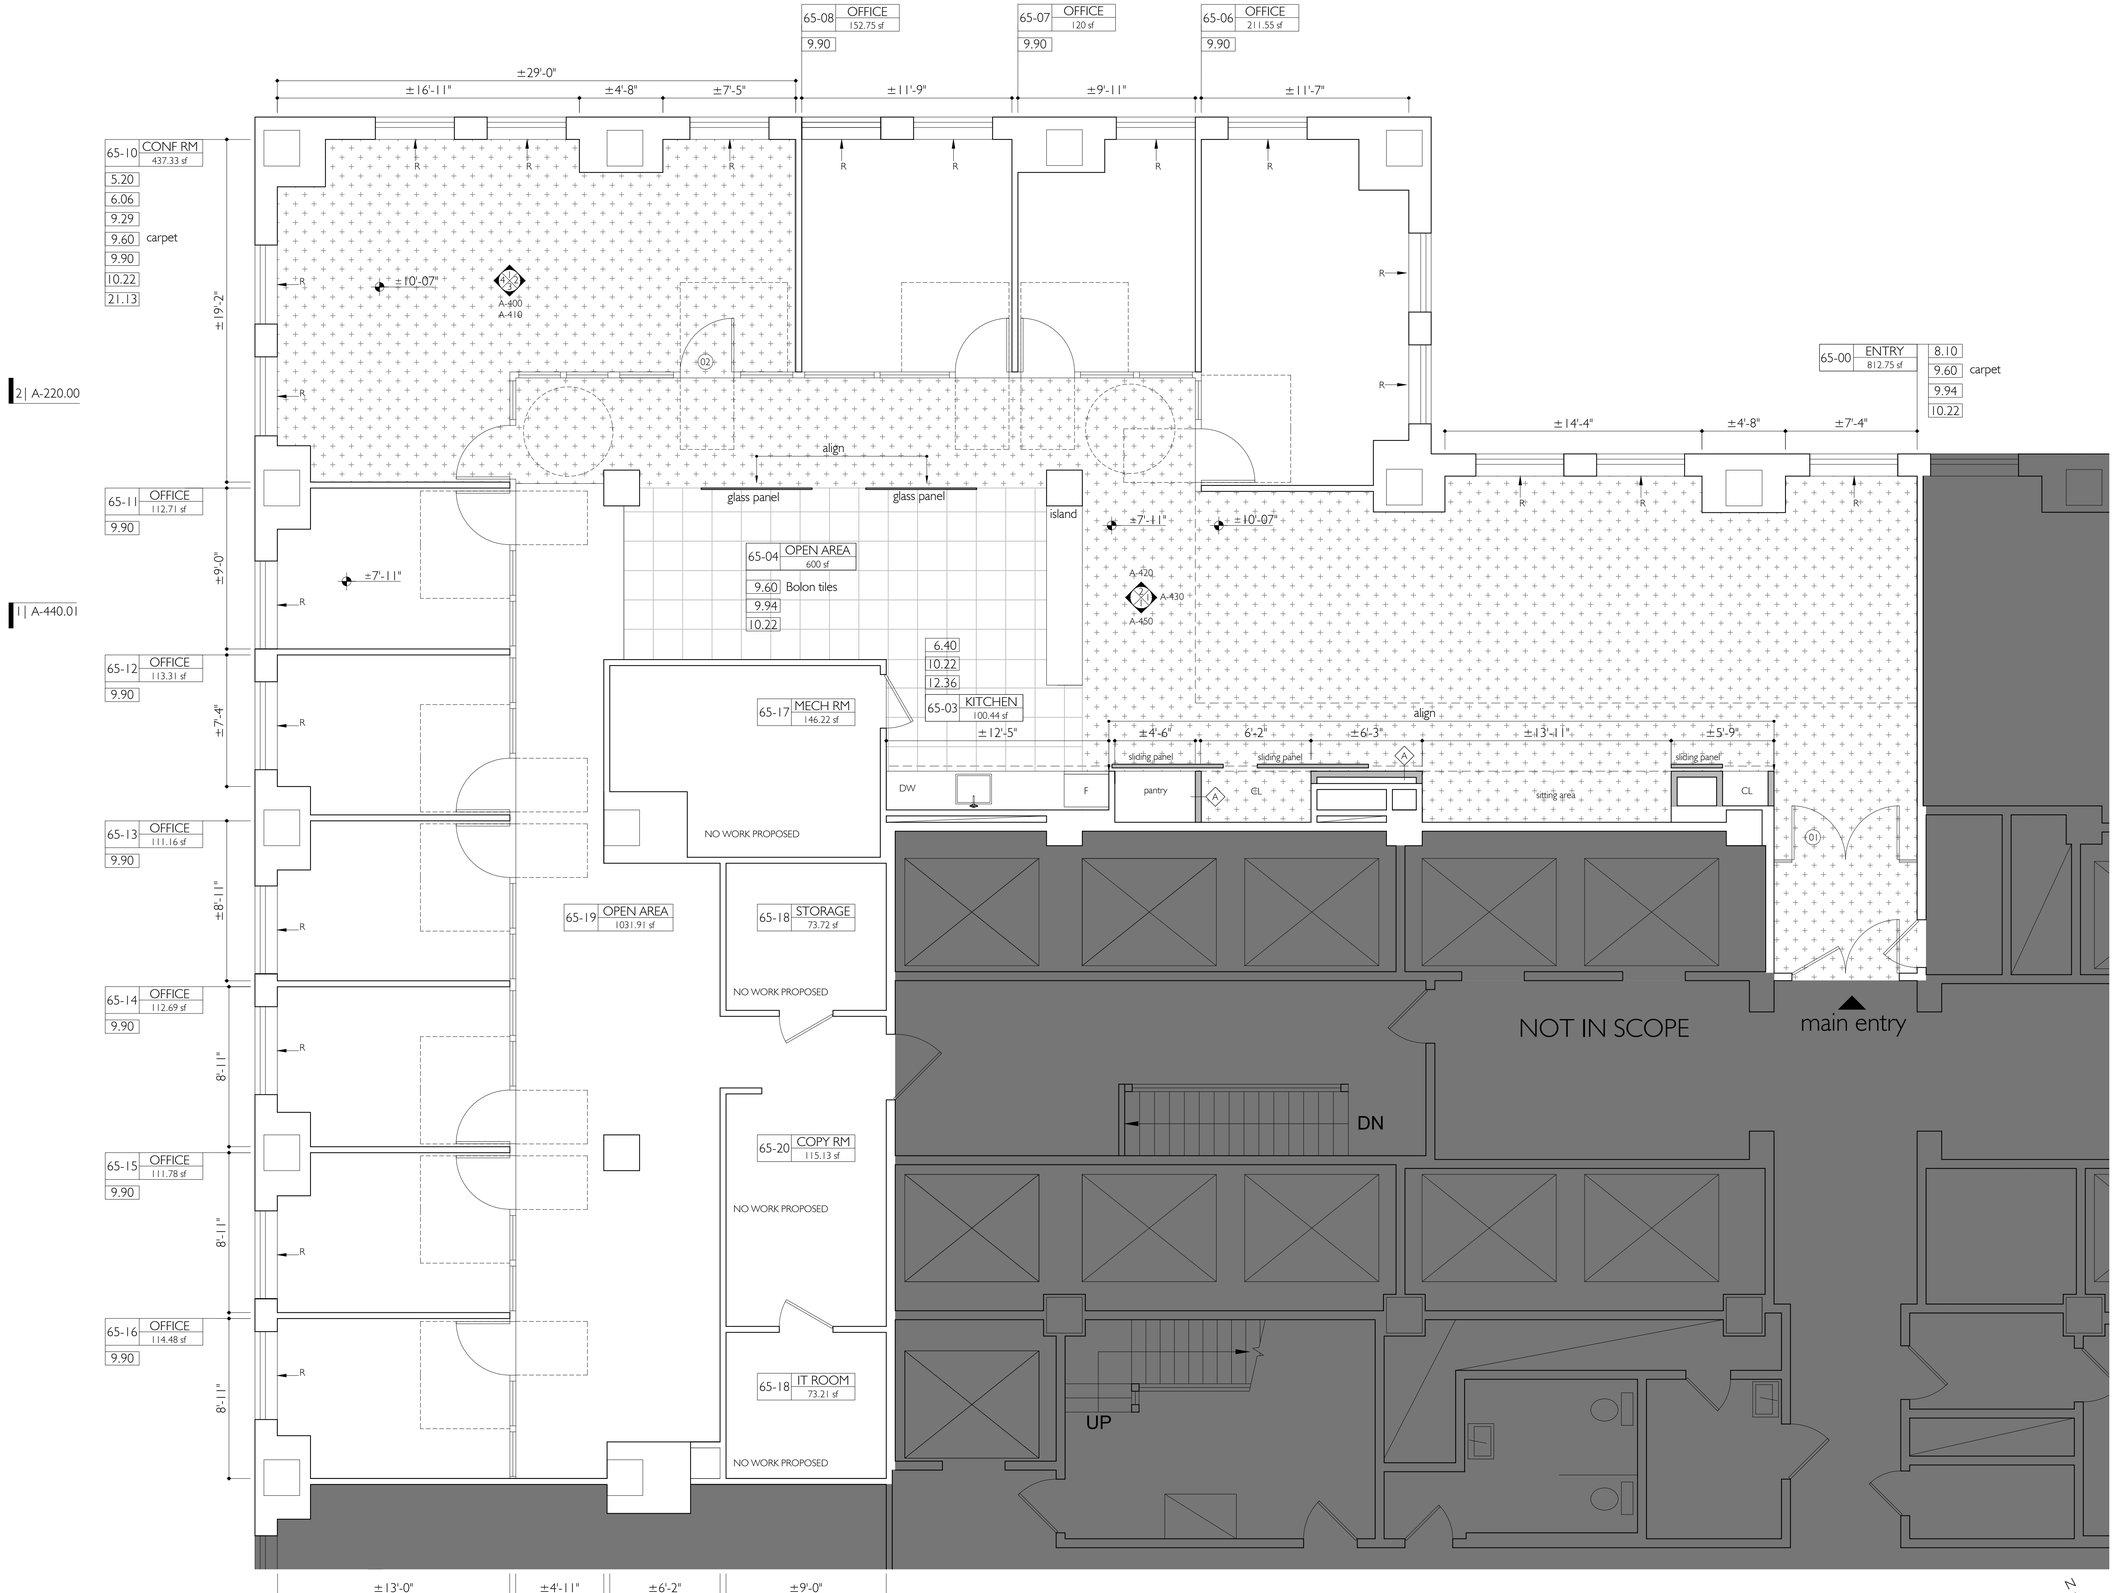

Proposed Floor 65 Partial Plan

Scale: ¼" = 1'-0"

LEGEND

- area not in scope
- indicates new
- carpet
- Bolon tiles
- ADA accessiblity
- door tag
- partition wall tag

ABBREVIATIONS

F	fridge
R	radiator
DW	dishwasher
±	verify in field

ARCHITECTURE

5.20	steel frame
6.06	plywood sheet
6.40	millwork
8.10	glass door
9.29	gypsum board
9.60	flooring
9.90	painting
9.94	decorative finish
10.22	partitions

MEP

21.13	sprinklers

06.14.17 FILING SET 7 of 19

dc ap pllc
david cunningham architecture planning
543 union st, 1c
brooklyn ny 11215
718 208 0815
www.dcapny.com

A-120.00

Proposed Floor 65 Partial Plans

AIMCO OFFICE

350 5th Avenue
New York, NY 10118